



August 2, 2021

Central Valley Regional Water Quality Control Board
1685 E St.
Fresno, CA 93706

Transmitted: Federal Express Overnight Mail

Electronic Mail to: centralvalleyfresno@waterboards.ca.gov and
Jeff.Robins@waterboards.ca.gov

**RE: Revised Form 200–Application/Report of Waste Discharge General–General Information
Form for Waste Discharge Requirements or NPDES Permit
EZ Trip #1277
44779 Lassen Ave.
Avenal, CA 93204**

Central Valley Regional Water Quality Control Board/Mr. Robins:

Dynamis, Inc. has been authorized by the facility owner and operator, Pilot Travel Centers LLC (Pilot) and the owner of the land, Interstate 5 Travel Center, Inc. to submit a revised Form 200 for the waste discharge for the current operating EZ Trip #1277 facility located at 44779 Lassen Ave., Avenal, CA 93204. On May 27, 2021, Form 200 and the annual fee check was submitted. On that Form 200, the owner of the land information was incorrect. We apologize for the error. I have been communicating with Mr. Jeff Robins of the Central Valley Water Quality Control Board (CVRWQCB) in Fresno, California regarding the revisions that needed to be made to Form 200. He indicated that owner of the land information needed to be corrected on Form 200. Both the owner of the land (Interstate 5 Travel Center, Inc.) and the facility owner and operator (Pilot Travel Centers LLC) must sign the application. This has been completed. See revised attached Form 200. A check in the amount of \$1,424 was submitted previously for the 2020-2021 annual fee for the current EZ Trip #1277 (former Interstate 5 Travel Center) with CVRWQCB assigned numbers WDID# 5C10NC00203 and Place ID 835076.

Thank you for your time and assistance. If you have any questions, please feel free to contact me at 865-588-5422 ext. 208 or at alanfass@dynamis-inc.com

Sincerely,

Alan J. Fass
Environmental Program Manager
Dynamis, Inc.
865-588-5422 Ext. 208
alanfass@dynamis-inc.com

Enclosures

- Revised Form 200–Application/Report of Waste Discharge General–General Information Form for Waste Discharge Requirements or NPDES Permit (with attachments)

Cc: Mr. Joey Cupp, Director of Environmental, Pilot Travel Centers LLC, 5508 Lonas Road, Knoxville, TN 37909 joey.cupp@pilottravelcenters.com
Mr. Chip Hughes, Environmental Project Manager, Pilot Travel Centers LLC, 5508 Lonas Road, Knoxville, TN 37909 chip.hughes@pilottravelcenters.com
Liz Peterson, Environmental Compliance Specialist, Pilot Travel Centers, LLC, 5508 Lonas Road, Knoxville, TN 37909 liz.peterson@pilottravelcenters.com
Mr. Geoff Steinbach, Interstate 5 Travel Center, Inc., 5382 North McCall Ave., Clovis, CA. 93619 g935@comcast.net
Mr. Jay Steinbach, Interstate 5 Travel Center, Inc., maxxchip@netzero.net

State of California
Regional Water Quality Control Board

APPLICATION/REPORT OF WASTE DISCHARGE
GENERAL INFORMATION FORM FOR
WASTE DISCHARGE REQUIREMENTS OR NPDES PERMIT

I. FACILITY INFORMATION

A. FACILITY:

Name EZ Trip #1277
Address 44779 Lassen Ave.
City/County/State/Zip Code Avenal, CA 93204
Contact Person Mr. Joey Cupp
Telephone Number 865-474-2826 Email joey.cupp@pilottravelcenters.com

B. FACILITY OWNER:

Name Pilot Travel Centers LLC
Address 5508 Lonas Drive
City/State/Zip Code Knoxville, TN 37909
Contact Person Mr. Joey Cupp
Telephone Number 865-474-2826 Email joey.cupp@pilottravelcenters.com
Federal Tax ID 34-1953155

Owner Type (*Mark one*):

☐ Individual ☒ Corporation ☐ Governmental Agency ☐ Partnership
☐ Other: _____

C. FACILITY OPERATOR (*The agency or business, not the person*):

Name Pilot Travel Centers LLC
Address 5508 Lonas Drive
City/State/Zip Code Knoxville, TN 37909
Contact Person Mr. Joey Cupp
Telephone Number 865-474-2826 Email joey.cupp@pilottravelcenters.com

Operator Type (*Mark one*):

☐ Individual ☒ Corporation ☐ Governmental Agency ☐ Partnership
☐ Other: _____

D. OWNER OF THE LANDName Interstate 5 Travel Center, Inc.Address 5382 North McCall Ave.City/State/Zip Code Clovis, CA 93619Contact Person Geoff SteinbachTelephone Number 559-259-7738Email g935@comcast.netOwner Type (*Mark one*):

- ☐ Individual ☒ Corporation ☐ Governmental Agency ☐ Partnership
☐ Other: _____

E. ADDRESS WHERE LEGAL NOTICE MAY BE SERVEDAddress Pilot Travel Centers LLC, 5508 Lonas DriveCity/State/Zip Code Knoxville, TN 37909Contact Person Mr. Joey CuppTelephone Number 865-474-2826Email joey.cupp@pilottravelcenters.com**F. BILLING ADDRESS**Address Pilot Travel Centers LLC, 5508 Lonas DriveCity/State/Zip Code Knoxville, TN 37909Contact Person Liz PetersonTelephone Number 865-474-3802Email Liz.Peterson@pilottravelcenters.com**II. TYPE OF DISCHARGE***Check Type of Discharge(s) Described in this Application:*☒ **Waste Discharge to Land**☐ **Waste Discharge to Surface Water***Check all that apply:*☐ Animal or Aquacultural Wastewater☐ Land Treatment Unit☐ Animal Waste Solids☐ Landfill (*see instructions*)☐ Biosolids/Residual☐ Mining☐ Cooling Water☐ Storm Water☒ Domestic/ Municipal Wastewater
Treatment and Disposal☐ Surface Impoundment☐ Dredge Material Disposal☐ Waste Pile☐ Hazardous Waste (*see instructions*)☐ Wastewater Reclamation☐ Industrial Process Wastewater☐ Other, *please describe* _____

III. LOCATION OF THE FACILITY

Describe the physical location of the facility:

1. Assessor's Parcel Number(s)

Facility: EZ Trip #1277 at 44779 Lassen Ave., Avenal, CA 93204

Discharge Point: Leach Field

2. Latitude

Facility: 36.072892 N

Discharge Point: 36.075865 N

3. Longitude

Facility: -120.102644 W

Discharge Point: -120.103991 W

IV. REASON FOR FILING

Check all that apply:

- ☐ New Discharge or Facility
- ☐ Change in Design or Operation
- ☐ Change in Quantity/Type of Discharge
- ☒ Changes in Ownership/Operator (see instructions)
- ☐ Waste Discharge Requirements Update or NPDES Permit Reissuance
- ☐ Other: _____

V. CALIFORNIA ENVIRONMENTAL QUALITY ACT (CEQA)

Name of Lead Agency _____

Has a public agency determined that the proposed project is exempt from CEQA?

☐ Yes ☐ No

If yes, state the basis for the exemption and the name of the agency supplying the exemption on the line below:

Has a "Notice of Determination" been filed under CEQA?

☐ Yes ☐ No

If Yes, enclose a copy of the CEQA document, Environmental Impact Report (EIR), or Negative Declaration. If No, identify the expected type of CEQA document and expected date of completion.

Expected CEQA Documents: ☐ EIR ☐ Negative Declaration

Expected CEQA Completion Date: _____

VI. OTHER REQUIRED INFORMATION

Please provide a COMPLETE characterization of your discharge. A complete characterization includes, but is not limited to, design and actual flows, a list of constituents and the discharge concentration of each constituent, a list of other appropriate waste discharge characteristics, a description and schematic drawing of all treatment processes, a description of any Best Management Practices (BMPs) used, and a description of disposal methods.

Also include a site map showing the location of the facility and, if you are submitting this application for an NPDES permit, identify the surface water to which you propose to discharge. Please try to limit your maps to a scale of 1:24,000 (7.5' USGS Quadrangle) or a street map, if more appropriate.

VII. OTHER

Attach additional sheets to explain any responses which need clarification. List attachments with titles and dates below:

VI. Other Required Information - Description of on-site wastewater treatment system & disposal methods

Delegation of Authority, Site Plan (6/24/2020), Utility Plan (6/22/2020)

On-Site Sewage Treatment System Design As-Built Site Plan (4/7/2020)

You will be notified by a representative of the RWQCB within 30 days of receipt of your application. The notice will state if your application is complete or if there is additional information you must submit to complete your Application/Report of Waste Discharge, pursuant to Division 7, Section 13260 of the California Water Code.

VIII. CERTIFICATION

"I certify under penalty of law that this document, including all attachments and supplemental information, were prepared under my direction and supervision in accordance with a system designed to assure that qualified personnel properly gathered and evaluated the information submitted. Based on my inquiry of the person or persons who manage the system, or those persons directly responsible for gathering the information, the information submitted is, to the best of my knowledge and belief, true, accurate, and complete. I am aware that there are significant penalties for submitting false information, including the possibility of fine and imprisonment."

Print Name JAY Steinbach Title President / Interstate 5 Travel Center
Signature [Signature] Date 7-29-21

FOR OFFICE USE ONLY

Date Form 200 Received:	Letter to Discharger:	Fee Amount Received:	Check #:
-------------------------	-----------------------	----------------------	----------

VI. OTHER REQUIRED INFORMATION

Please provide a COMPLETE characterization of your discharge. A complete characterization includes, but is not limited to, design and actual flows, a list of constituents and the discharge concentration of each constituent, a list of other appropriate waste discharge characteristics, a description and schematic drawing of all treatment processes, a description of any Best Management Practices (BMPs) used, and a description of disposal methods.

Also include a site map showing the location of the facility and, if you are submitting this application for an NPDES permit, identify the surface water to which you propose to discharge. Please try to limit your maps to a scale of 1:24,000 (7.5' USGS Quadrangle) or a street map, if more appropriate.

VII. OTHER

Attach additional sheets to explain any responses which need clarification. List attachments with titles and dates below:

VI. Other Required Information - Description of on-site wastewater treatment system & disposal methods

Delegation of Authority, Site Plan (6/24/2020), Utility Plan (6/22/2020)

On-Site Sewage Treatment System Design As-Built Site Plan (4/7/2020)

You will be notified by a representative of the RWQCB within 30 days of receipt of your application. The notice will state if your application is complete or if there is additional information you must submit to complete your Application/Report of Waste Discharge, pursuant to Division 7, Section 13260 of the California Water Code.

VIII. CERTIFICATION

"I certify under penalty of law that this document, including all attachments and supplemental information, were prepared under my direction and supervision in accordance with a system designed to assure that qualified personnel properly gathered and evaluated the information submitted. Based on my inquiry of the person or persons who manage the system, or those persons directly responsible for gathering the information, the information submitted is, to the best of my knowledge and belief, true, accurate, and complete. I am aware that there are significant penalties for submitting false information, including the possibility of fine and imprisonment."

Print Name Joey Cupp

Title Director, Environmental

Signature 

Date 7-30-21

*See attached Delegation of Authority

FOR OFFICE USE ONLY

Date Form 200 Received:	Letter to Discharger:	Fee Amount Received:	Check #:
----------------------------	--------------------------	-------------------------	----------

Attachment

VI. Other required Information--description of onsite waste water treatment system & disposal methods

The EZ Trip #1277 travel center facility located at 44779 Lassen Ave., Avenal, CA operates 24 hours a day, 365 days a year as a travel stop for automobiles, commercial trucks, recreational vehicles, and buses. The travel center contains a main commercial building that has a retail convenience store, restaurant, restrooms, and multiple shower rooms for professional truck drivers and other patrons. There are two fuel filling areas. The fueling area for trucks and buses is located south of the main building. The fueling area for automobiles and light duty trucks is located north of the main building.

Domestic wastewater is generated from the restrooms, showers, food preparation and dishwashing operations from restaurant and fast food service operations, laundry, and cleaning. Water meter readings for the travel center indicate an average water use of approximately 11,000 gallons per day (gpd) as calculated for 5 months from 11/1/2020 to 4/1/2021, but that water use can peak up to 15,000 gpd during peak operating days, weekends, and holidays. The existing onsite wastewater treatment system reportedly consists of:

- 1,500-gallon grease interceptor;
- 8,000-gallon septic tank;
- 4-inch sewer pipe from travel center main building to the 30,000 gallon primary septic tank with 6 inch sewer pipe leaving tank and connected to 15,000 gallon secondary tank with aeration;
- 15,000-gallon surge/pump tank with an Orenco Duplex pump system with dual Orenco effluent pump package;
- 1.5" Sch 40 PVC piping;
- 1.5" flow meter;
- Automated timed pressure dosing of wastewater to the leachfield;
- The effluent is discharged from the surge tank into a 1,000-linear foot leachfield with ten 100-foot laterals in 2 zones;
- Flow equalizer valve box;
- Inspection ports; and
- Flushing valve box.

See attached On-Site Sewage Treatment System Design As-Built Plan, dated April 7, 2020 which was installed (or was existing) under the former facility owner and operator.

The food grease interceptor will be pumped out as needed by a licensed grease trap service vendor. The septic tanks will be pumped out as needed by a licensed pump and haul service contractor.

Sources of information came from the attached On-Site Sewage Treatment System Design As-Built Plan, dated April 7, 2020, by which the system was upgraded by the former facility owner and operator; and a review of a Central Valley Regional Water Quality Board Technical Memorandum dated March 9, 2018 for the former owner and facility named Interstate Travel Center, Onsite Wastewater Treatment System, Fresno County. Pilot Travel Centers LLC currently operates the facility under the name, EZ Trip #1277.

There is an existing California Regional Water Quality Control Board--Central Valley Region Monitoring and Reporting Program No. 2014-01523-DWQ-R5232 for the former owner & facility operator, Jay Steinbach

for Interstate Travel Center Onsite Waste Water Treatment System, Fresno, County. Pilot Travel Centers LLC is requesting a change in ownership by submittal of this Form 200. And when approved, Pilot will presumably receive a California Regional Water Quality Control Board—Central Valley Region Monitoring and Reporting Program No. document.

DELEGATION OF AUTHORITY

Granted to

JOEY CUPP

Effective January 1, 2021

Expires December 31, 2021

Acting pursuant to sections 8.08, 9.01 and 9.03 of the Sixth Amended and Restated Limited Liability Agreement of Pilot Travel Centers LLC (the “Company”), the undersigned, Kevin Wills, Chief Financial Officer, does hereby delegate to Joey Cupp, Director of Environmental, for the period hereinafter specified, the power and authority, in addition to and not in limitation of any other power and authority he may have, acting alone and subject to the restrictions and limitations set forth herein, to sign Environmental documents and to enter into commitments and to negotiate, execute, deliver, and perform under contracts and do and perform all such other acts and things on behalf of and in the name of the Company, as are necessary and appropriate to accomplish the management, business, and affairs of the Company in the ordinary course of business, subject in any case and in all matters to (i) the control of the CEO, CFO or other officer of the Company and (ii) the right of the CEO, CFO or other officer of the Company to revoke this power and authority upon written notice to Joey Cupp, a copy of which notice shall be duly filed with the Secretary of the Company (“Delegation”).

Joey Cupp is hereby authorized, acting singly, unless provided otherwise below, to negotiate, execute, acknowledge, deliver, and perform under, in the ordinary course of the Company’s business, as are necessary and appropriate to accomplish the management, business and affairs of the company in the ordinary course of business subject in any case and in all matters relating to the Environmental Documents which are prepared in the regular course of business.

Joey Cupp is further authorized to execute, acknowledge, deliver and perform under, in the ordinary course of business, not by limitation but by way of confirmation, the following types of documents:

1. Tank Registrations
2. Tank Notifications
3. Reimbursement Applications
4. Soil and Groundwater Classifications
5. Site Assessment Reports

6. Corrective Action Plans
7. Operating Permits
8. Discharge Monitoring Reports (NPDES) Permit Monitoring
9. Transfer and accept permits

Provided, however, nothing contained in this power shall authorize Joey Cupp to (i) underwrite, warrant, endorse or guarantee the performance, obligation, or other similar undertaking of any person, Company or other entity whatsoever other than subsidiary Companies of the Company; (ii) purchase, sell, convey, exchange or lease real estate, except as expressly provided above; or (iii) underwrite, warrant, endorse or guarantee the debt obligation of any person, Company or other entity whatsoever.

Joey Cupp shall be authorized to act for all the facilities listed in the attached Exhibit A and those in the future that are owned or operated by Pilot Travel Centers LLC. In the event additional facilities have been added and this Delegation of Authority is still in full force and effect, Joey Cupp in his position as Director of Environmental, shall have the authority to notify each representative State of any additional facilities covered by this Delegation of Authority by a letter addressed to the appropriate department and shall have all the rights assigned to him under this Delegation of Authority in full force and effect as if first above stated herein on Exhibit A until the expiration of this Delegation of Authority.

Joey Cupp shall be authorized to act hereunder from the effective date hereof only so long as he shall remain an employee of the Company or until such time as this instrument has been revoked, annulled, and set aside by an instrument of revocation filed with the Secretary of the Company, or until December 31, 2021, whichever may first occur.

A photocopy of this Delegation of Authority shall serve as the original.

IN WITNESS WHEREOF, Kevin Wills, the duly authorized President of the Company, has executed this Delegation of Authority in the County of Knox, State of Tennessee, February 3, 2021, but effective as of January 1, 2021.

ATTEST:

DocuSigned by:

114ACBE580224EA...
Kevin Wills
Chief Financial Officer

DocuSigned by:

0A5DFEA43730447...
Kristin K. Seabrook
Secretary

CONSTRUCTION NOTES


- 01 EXISTING CONVENIENCE STORE BUILDING TO BE REMODELED (SEE ARCHITECTURAL DRAWINGS), INSTALLED BY CONTRACTOR.
- 02 EXISTING AUTO CANOPY TO BE RE-IMAGED BY CANOPY SUPPLIER.
- 03 EXISTING TRUCK CANOPY TO BE RE-IMAGED BY CANOPY SUPPLIER.
- 04 34'-0" x 28'-4" TRUCK CANOPY ADDITION, FURNISHED AND INSTALLED BY CANOPY SUPPLIER. CANOPY FOUNDATIONS INSTALLED BY CONTRACTOR.
- 05 44'-10" x 39'-0" 8" REINFORCED CONCRETE PAD FOR TRUCK CANOPY ADDITION, INSTALLED BY CONTRACTOR.
- 06 NEW CONCRETE ISLAND WITH A DIESEL DISPENSER AND CONTAINMENT BOX TYPICAL AT (2) PLACES, INSTALLED BY CONTRACTOR.
- 07 EXISTING SITE LIGHT POLE TO BE RELOCATED AS REQUIRED FOR INSTALL OF NEW UNDERGROUND STORAGE TANK.
- 08 TANK #1, 2, 3, & 4, EXISTING UNDERGROUND GASOLINE AND DIESEL STORAGE TANKS, NOT TO BE DISTURBED. SEE PRODUCT PIPING DRAWINGS FOR EXTENT OF MODIFICATIONS.
- 09 TANK #5, 6, 7, & 8, EXISTING ABOVEGROUND DIESEL STORAGE TANKS, NOT TO BE DISTURBED. SEE PRODUCT PIPING DRAWINGS FOR EXTENT OF MODIFICATIONS.
- 10 TANK #9 & 10, PRODUCT #3, NEW 12,000 GALLON UL 142 DOUBLE-WALL STEEL ABOVEGROUND DIESEL STORAGE TANKS (21'-8" x 10'-0") FURNISHED BY PILOT, INSTALLED BY CONTRACTOR. (SEE PP DRAWINGS FOR MORE INFORMATION).
- 11 TANK #11 & 12, PRODUCT #4, NEW 12,000 GALLON UL 142 DOUBLE-WALL STEEL ABOVEGROUND 999 STORAGE TANKS (21'-8" x 10'-0") FURNISHED BY PILOT, INSTALLED BY CONTRACTOR. (SEE PP DRAWINGS FOR MORE INFORMATION).
- 12 TANK #13, PRODUCT #5, 12,000 GALLON, 8'-0" x 37'-0 1/2" LONG, DOUBLE-WALL FIBERGLASS UNDERGROUND DIESEL EXHAUST FLUID (DEF) TANK, FURNISHED BY OWNER, INSTALLED BY CONTRACTOR. SEE PP DRAWINGS FOR MORE INFORMATION. (TYP. (1) PLACE).
- 13 899 INJECTION SHED WITH SUMP, SUPPLIED BY OWNER. (SEE PRODUCT PIPING DRAWINGS FOR MORE INFORMATION).
- 14 SITE LIGHT, FURNISHED BY OWNER, INSTALLED BY CONTRACTOR. (SEE SHEET C5.2)
- 15 EXISTING TRUCK SCALE TO BE REMOVED (SEE SHEET C2). PIT TO BE INFILLED AS REQUIRED AND PREPARED FOR INSTALLATION OF NEW HEAVY DUTY TRUCK ASPHALT PAVING. SEE DETAILS ON SHEET C5.1.
- 16 NEW TRUCK SCALE, CONCRETE TRUCK SCALE PIT AND TRUCK SCALE FURNISHED AND INSTALLED BY TRUCK SCALE SUPPLIER. ELECTRICAL, COMMUNICATIONS AND DRAINAGE PROVIDED TO THE SCALE PIT BY CONTRACTOR, COORDINATION BY CONTRACTOR.
- 17 NO NEW IMPROVEMENTS REQUIRING ELECTRIC TO BE INSTALLED WITHIN 25' OF EXIST. PROPANE TANK.
- 18 TRASH ENCLOSURE 8' CHAIN LINK FENCE WITH VINYL INSERTS MOUNTED ON 8" REINFORCED CONCRETE PAD WITH PROTECTIVE STEEL BOLLARDS, INSTALLED BY CONTRACTOR (SEE ARCH DWGS FOR DETAILS).
- 19 TRASH COMPACTOR, FURNISHED AND INSTALLED BY TRASH COMPACTOR SUPPLIER.
- 20 CARDBOARD BAILER OR RECYCLE DUMPSTER, FURNISHED AND INSTALLED BY DUMPSTER SUPPLIER.
- 21 GREASE CONTAINER, PROVIDED BY OWNER.
- 22 4" STEEL PIPE BOLLARD FURNISHED, INSTALLED BY CONTRACTOR (SEE CML DWGS FOR SPECS.).
- 23 TRUCK AIR STAND, TYPICAL AT EVERY OTHER TRUCK FUELING ISLAND, SUPPLIED BY OWNER AND INSTALLED BY CONTRACTOR.
- 24 TRUCK FREEZE PROOF WATER STAND TYPICAL AT EVERY OTHER TRUCK FUELING ISLAND FURNISHED AND INSTALLED BY CONTRACTOR.
- 25 EXISTING PROPANE TANKS, NOT TO BE DISTURBED.
- 26 DEF LED PRICER SIGN FURNISHED BY OWNER, INSTALLED BY SIGN SUPPLIER. ELECTRICAL INSTALLED BY CONTRACTOR.
- 27 PAINTED (SAFETY YELLOW) PARALLEL STRIPES AT 16" O.C. FURNISHED AND INSTALLED BY CONTRACTOR.
- 28 "PASSENGER LOADING ZONE ONLY" SIGN FURNISHED AND INSTALLED BY CONTRACTOR.
- 29 EXISTING INTERNALLY ILLUMINATED HI-RISE SIGN TO BE REFACED, INSTALLED BY SIGN SUPPLIER.
- 30 EXISTING INTERNALLY ILLUMINATED MONUMENT SIGN TO BE REFACED, INSTALLED BY SIGN SUPPLIER.
- 31 "TRUCK SCALE" INTERNALLY ILLUMINATED SIGN FURNISHED AND INSTALLED BY TRUCK SCALE SUPPLIER. CONCRETE FOUNDATION BY TRUCK SCALE SUPPLIER, ELECTRICAL PROVIDED TO SCALE BY CONTRACTOR.
- 32 "TRUCK ENTRANCE ONLY" (INTERNALLY ILLUMINATED) DIRECTIONAL SIGN FURNISHED BY OWNER, INSTALLED BY SIGN SUPPLIER. CONCRETE FOUNDATION AND ELECTRICAL (SOLAR POWERED) INSTALLED BY CONTRACTOR.
- 33 "TRUCKS ENTRY/EXIT" (INTERNALLY ILLUMINATED) DIRECTIONAL SIGN FURNISHED BY OWNER, INSTALLED BY SIGN SUPPLIER. CONCRETE FOUNDATION AND ELECTRICAL (SOLAR POWERED) INSTALLED BY CONTRACTOR.
- 34 NEW "RV AND BUS EXIT ONLY" SIGN TO REPLACE EXISTING SIGN FURNISHED BY OWNER, INSTALLED BY SIGN SUPPLIER. (NON-ILLUMINATED)
- 35 EXISTING FIRE HYDRANT TO REMAIN
- 36 NEW AUTO ASPHALT PAVING AT EXISTING RV DRIVE WAY. SEE DETAILS ON SHEET C5.1.
- 37 EXISTING SITE LIGHT POLE TO BE REPLACED.
- 38 EXISTING AUTO AIR/VACUUM, TO REMAIN.
- 39 EXISTING STRIPING TO BE REMOVED AND RE-STRIPED. ALL DIRECTIONAL AND PARKING STRIPING TO BE SAFETY YELLOW-UNLESS NOTED OTHERWISE (TYP.).
- 40 6" STEEL PIPE BOLLARD FURNISHED, INSTALLED BY CONTRACTOR. SEE DETAIL SHEET C8.0

- 41 INSTALL DIRECTIONAL ARROW. ALL DIRECTIONAL AND PARKING STRIPING TO BE SAFETY YELLOW-UNLESS NOTED OTHERWISE (TYP.).
- 42 INSTALL TACTILE WARNING DEVICE PER 11, SHEET A5.1. TO BE 3" DEEP
- 43 INSTALL (3) ADA ACCESSIBLE PARKING STALL, INCLUDING (1) VAN ACCESSIBLE. ALL ADA PARKING STALLS TO INCLUDE WHEEL STOPS PER DETAIL SHEET C5.1, ISA PAINTED AT REAR OF STALL, AND CA R99C (CA) SIGN. SEE DETAIL 1, SHEET C8.0
- 44 INSTALL "DO NOT ENTER" SIGN
- 45 INSTALL NEW CONCRETE WALKWAY AT END OF TRUCK CANOPY
- 46 REPLACE DOORS ON EXIST. DUMPSTER ENCLOSURE
- 47 INSTALL 20'x10' PULL-UP SPACE AND 20'x5' ACCESS AISLE
- 48 INSTALL NEW PRE CAST CONCRETE WHEEL STOP PROVIDED AND INSTALLED BY CONTRACTOR. SEE DETAIL 13/C5.2 FOR MORE INFORMATION.
- 49 INSTALL 2'0" CURB CUT
- 50 INSTALL 6" - 12" RIP RAP, ON GEOTEXTILE FABRIC
- 51 SITE LIGHT TO BE RELOCATED APPROX. 10' EAST OF ORIGINAL LOCATION. INSTALL NEW POLE & FIXTURE
- 52 3" BOLLARD TO BE INSTALLED APPROX. 3' DUE SOUTH OF THE LIGHT. SEE DETAIL SHEET C8.0
- 53 INSTALL/REFRESH RED PAINT ON CURBING AROUND FIRE HYDRANTS
- 54 INSTALL ROAD STRIPING & MARKINGS FOR FIRE LANE
- 55 EXIST. SEPTIC TANK. SEE SEPARATE PLANS FOR SEPTIC SYSTEM.
- 56 APPROXIMATE LOCATION OF LEACH FIELD BY OTHERS.

LEGEND	
STANDARD CURB & GUTTER	CONCRETE
HEAVY DUTY CURB AND GUTTER	NO PARKING AREA STRIPING
PROPERTY LINE	CHAIN LINK FENCE
PROPOSED PARKING STALLS	PROPOSED BLDG & PERMIT #
SITE INFORMATION	
PARKING	PROVIDED
AUTO PARKING	74
HANDICAP PARKING	03
TRUCK PARKING	65
ACRAGE - 38.01 ACRES	
ADN - 085-130-265	
SITE AND BUILDING ACCESSIBILITY PER ANSI A117.1	

FLOOD ZONE NOTE

THE FLOOD ZONE LIMIT LINE IS APPROXIMATED PER FIRM MAP NO. 05019C3450H DATED FEBRUARY 18, 2006. THE BASE FLOOD ELEVATION (BFE) IS NOT STATED FOR ZONE A.

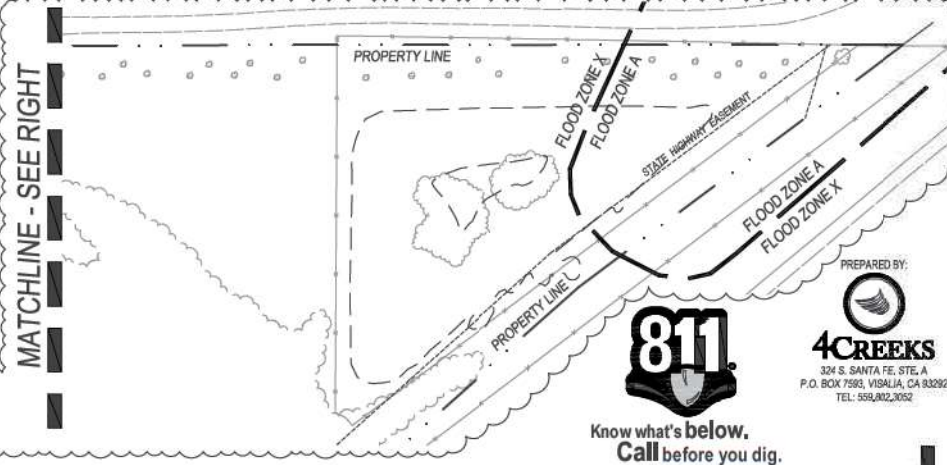

PILOT COMPANY
DESIGN DEPARTMENT
5508 LONAS ROAD
KNOXVILLE, TENNESSEE 37909
(865) 588-7488



PILOT TRAVEL CENTER
44779 LASSEN AVE.
AVENAL, CALIFORNIA 93204

DATE	REV.	REVISION DESCRIPTION	INT.	APP.	DATE
3/4/20	1	COUNTY COMMENTS			
6/15/20	2	GRADING COMMENTS			

SHEET:

C3.0




DATE	REV.	REVISION DESCRIPTION	INT.
6/1/20	1	COUNTY COMMENTS	MJR
6/15/20	2	GRADING COMMENTS	MJR

DATE: 3/4/20 DRAWN BY: VAB PROJECT: 1277-01
COPYRIGHT 2020 (P&H) PILOT COMPANY
THIS DRAWING IS A PROFESSIONAL ENGINEERING DESIGN AND IS NOT TO BE USED FOR ANY OTHER PURPOSE WITHOUT THE WRITTEN PERMISSION OF PILOT COMPANY.



UTILITY PLAN CONSTRUCTION NOTES

- CONTRACTOR TO INSTALL (4) 3/4" PEX WATER LINES INSIDE OF 2" PVC SLEEVES FROM EXISTING WATER METER TO TRUCK FREEZE PROOF WATER STAND (FURNISHED AND INSTALLED BY CONTRACTOR) LOCATED AT EVERY OTHER TRUCK FUELING ISLAND (TYP. (4) PLACES). PEX AND PVC SLEEVE TO BE PROVIDED AND INSTALLED BY CONTRACTOR. SEE CIVIL SHEETS FOR DETAILS.
- CONTRACTOR TO INSTALL 1/2" COPPER AIR LINE FROM AIR COMPRESSOR TO THE TRUCK AIR STAND LOCATED AT EVERY OTHER TRUCK FUELING ISLAND (TYP. (4) PLACES). SEE TC SHEETS FOR DETAILS.
- INSTALL ROOF LEADER AT CANOPY COLUMN WITH OUTLET AT GRADE. TYP. OF (4) NEW COLUMNS.
- REPLACE EXIST. 4" SANITARY SEWER LINE WITH 6" SCHEDULE 40 PVC PIPE AND CONNECT TO EXISTING SEPTIC SYSTEM. APPROXIMATE LOCATION SHOWN. CONTRACTOR TO VERIFY. CONTRACTOR TO CHECK INVERT AT "Y" (SEE PLUMBING PLANS FOR "Y" INVERT) AND VERIFY ADEQUATE FALL IS PROVIDED TO SEPTIC TANK (SLOPE=0.0050 MIN. 0.0100 PREFERRED) AND NOTIFY PILOT SUPERINTENDENT IMMEDIATELY IF FOUND TO BE INADEQUATE.
- INSTALL VALVE BOX W/ (4) WATER VALVE, (1) @ EA. PEX WATER LINE.
- PROTECT IN PLACE EXIST. UNDERGROUND ELECTRIC LINES EXCEPT AS NOTED OTHERWISE PER M.E.P. PLANS
- INSTALL FIRE DEPARTMENT CONNECTION WITHIN 50' OF EXIST. HYDRANT
- INSTALL 6" C900 FIRE LINE TO BUILDING. VERIFY FIRE RISER LOCATION WITH PLUMBING PLANS

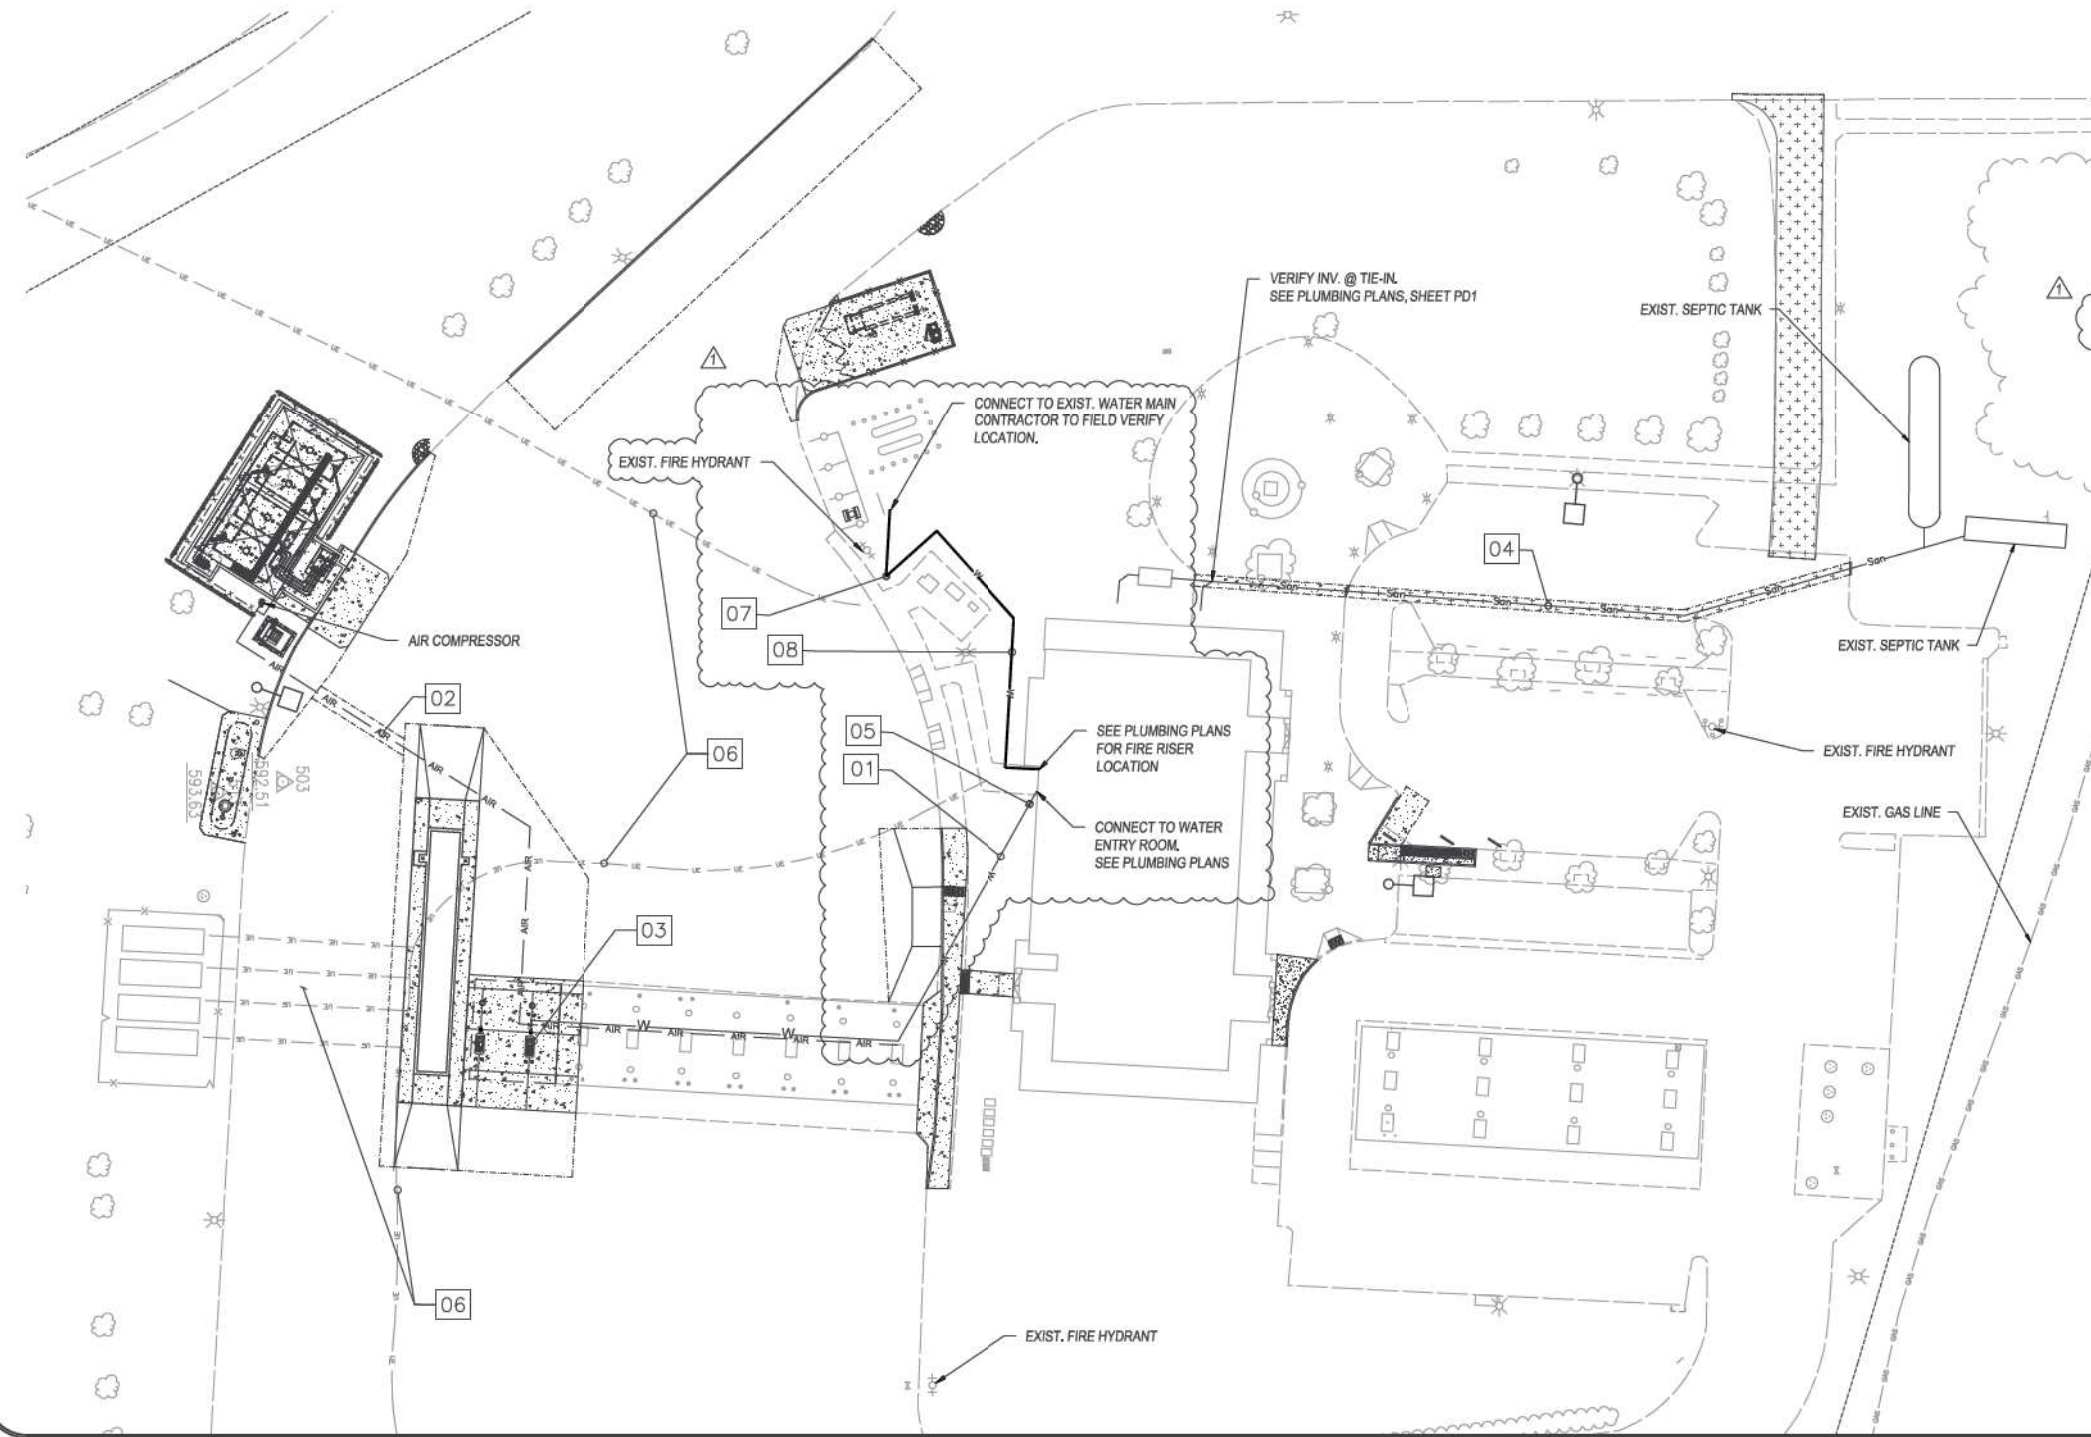

On-Site Sewage Treatment
System Design As-Built Site Plan

For:

Hillcrest Travel Plaza
44779 Lassen Ave
Avenal CA 93204

SCALE: 1" = 50'

By:

O.S.T. System Designs, Inc.
Armando G. Flores, REHS
PO Box 274
Biola CA 93606
559.288.8494

Installed & Maintained by:

BC Construction
Robert Coltra
209-628-5137

